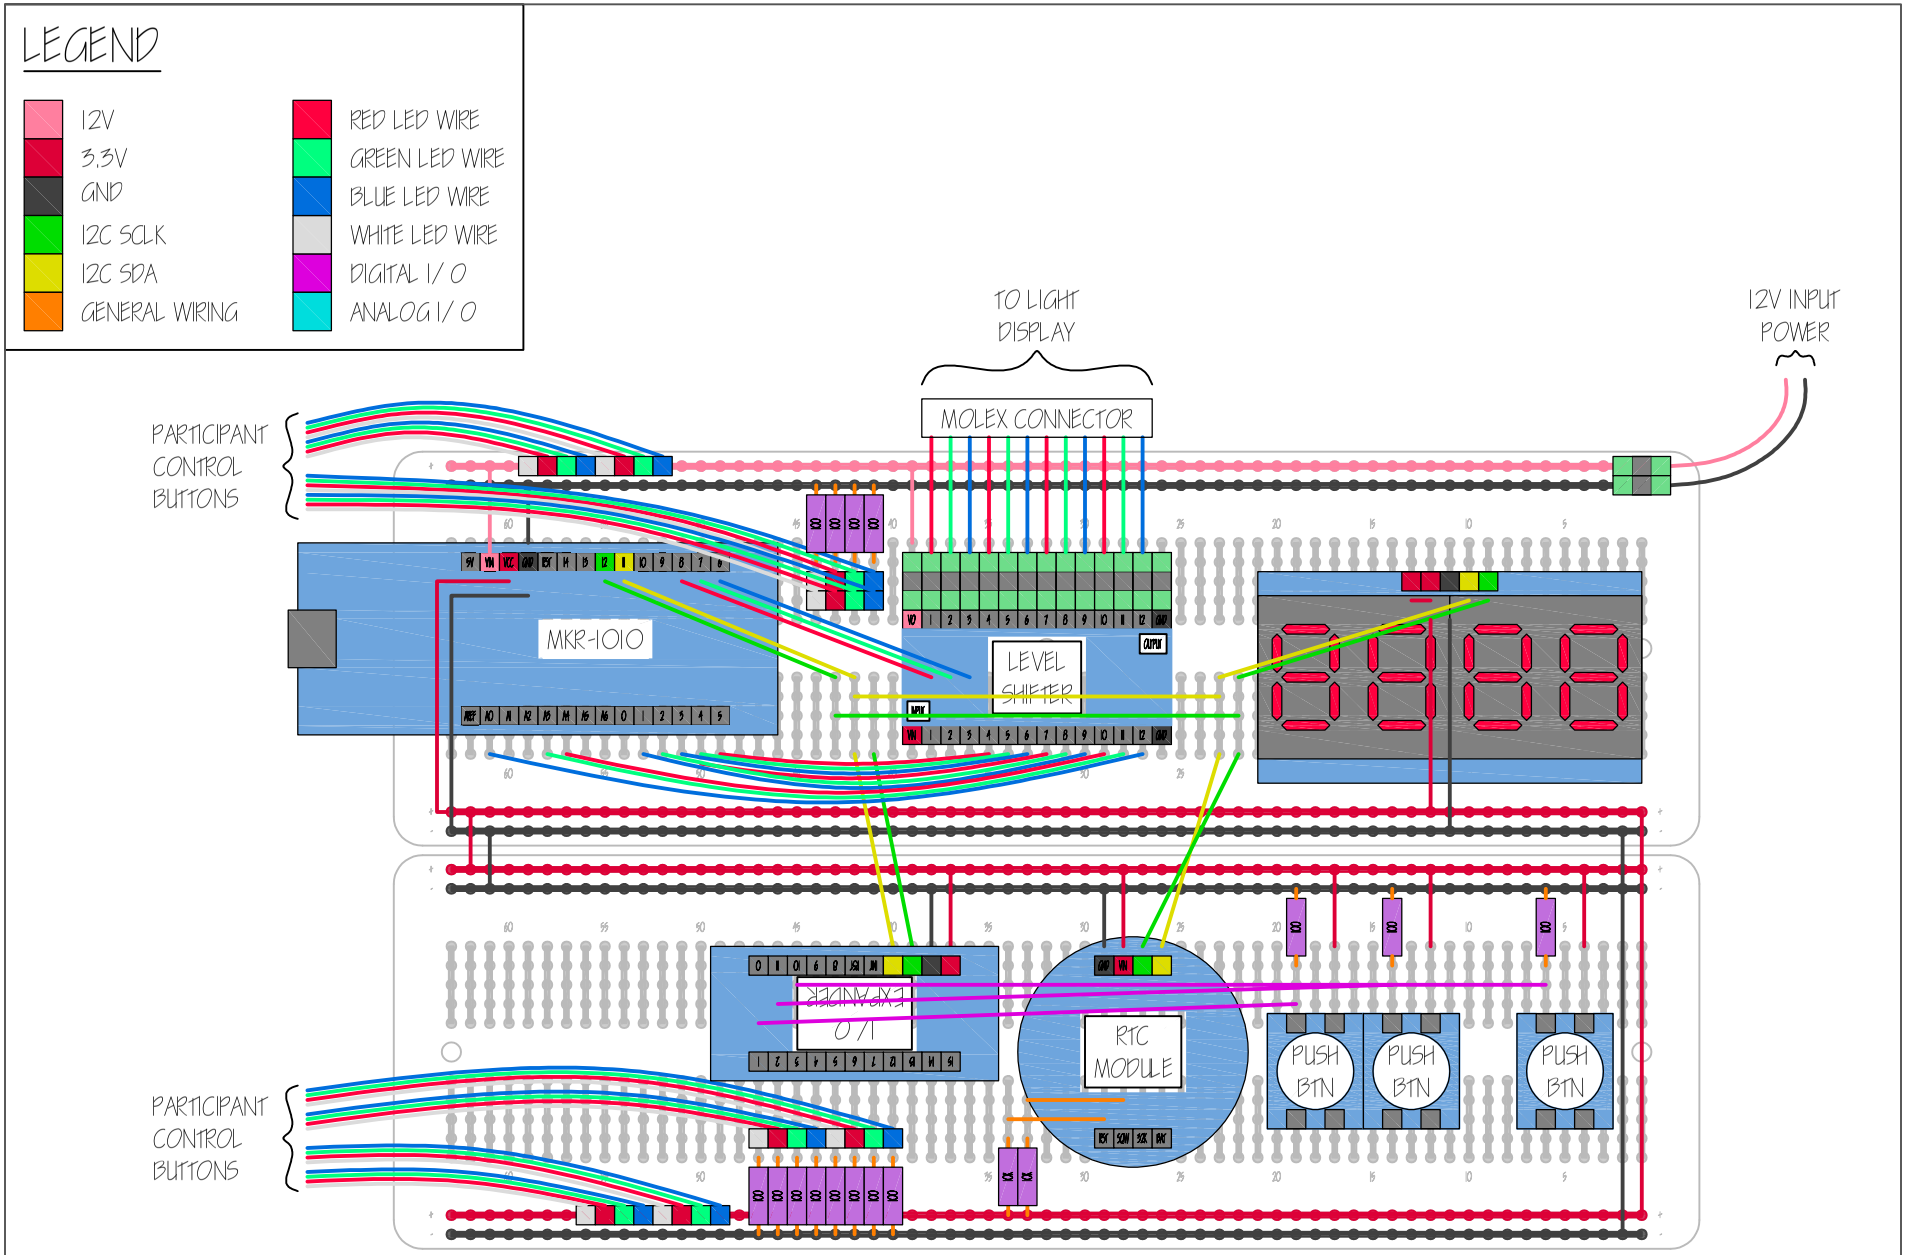

BREADBOARD LAYOUT

BREADBOARD LAYOUT	
LAGOMORPHIC CONSTRUCTS	
JULY 2024	REV -